


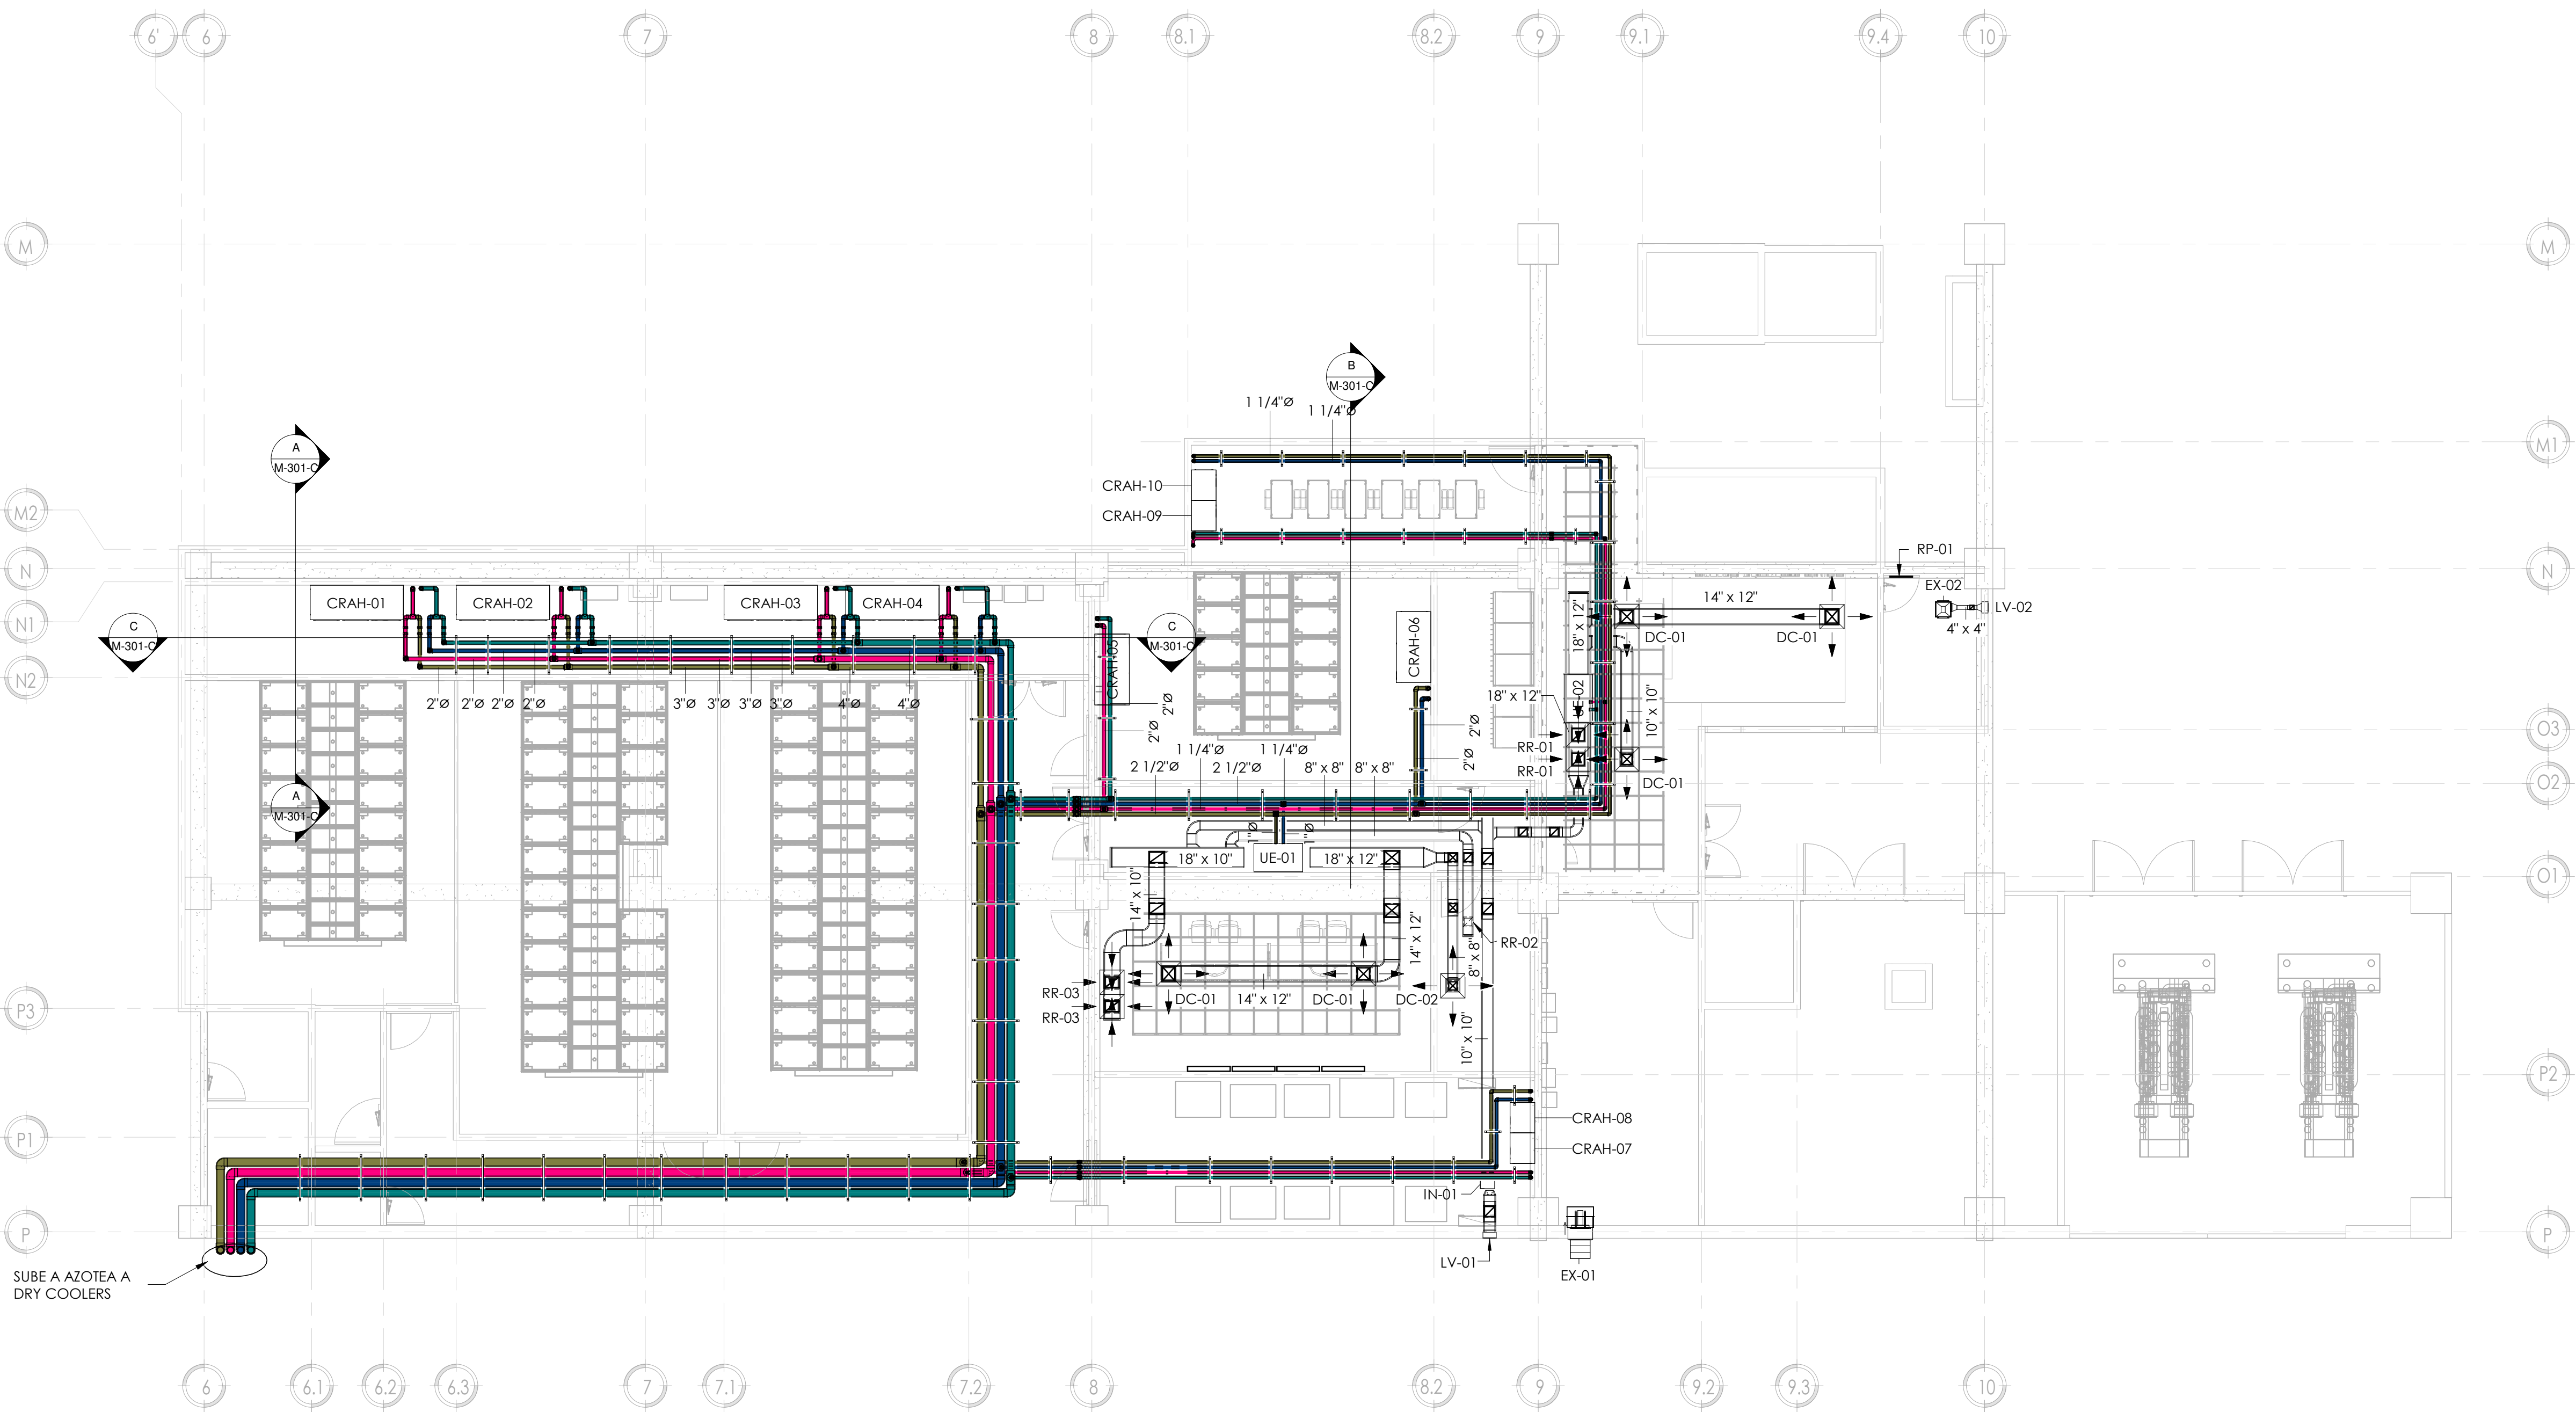

1 PLANTA DE AIRE ACONDICIONADO N1
ESCALA: 1 : 100

TITULOS

PROYECTO

DATA CENTER HND
CENTRO CIVICO

PROPIETARIO


GOBIERNO DE LA
REPÚBLICA DE HONDURAS
★ ★ ★ ★ ★

ANTEPROYECTO

INGENIUM BY DCC

CONTENIDO

PLANTA DE AIRE ACONDICIONADO N1

DISEÑO


data center intelligence
Oficinas Sigma Business Center, Piso 1
San Pedro, San José, Costa Rica
Teléfono: +506 2291 3454 / www.ingeniumla

PROFESIONALES RESPONSABLES

DISEÑO ARQUITECTONICO	COD A-28402	DIRECCION TECNICA	COD IM-19443
Ara. Ligia Cabalceta Vega		Ing. Marisol Jiménez Méndez	
DISEÑO ELECTRICO	COD IM-24751	DISEÑO MECANICO	COD IM-18397
Ing. Gloriana Jiménez León		Ing. Edgar José Aguilar Durán	
DISEÑO ESTRUCTURAL	CND ---		

NOTA

EL AUTOR SE RESERVA LA PROPIEDAD INTELECTUAL SOBRE LOS PLANOS Y SU CONTENIDO. LOS PLANOS NO DEBERÁN SER MODIFICADOS Y SOLO PODRÁN SER USADOS PARA LA CONSTRUCCIÓN DE LA OBRA PROYECTADA.
LAS REFERENCIAS A MARCAS O PRODUCTOS PARTICULARES DE NINGUNA MANERA LIMITA O EXCLUYE LA POSIBILIDAD DE UTILIZAR PRODUCTOS DE OTRAS MARCAS O PROVEEDORES. SIEMPRE QUE SEAN SIMILARES AL DE LA REFERENCIA Y CUMPLAN CON LAS MISMAS ESPECIFICACIONES.

REVISIONES

#	DESCRIPCION	APRUEBA	FECHA

ESCALA INDICADA

DEPARTAMENTO	MUNICIPIO	PAIS
TEGUCIGALPA	---	HONDURAS
NOVIEMBRE 2018		

PLANO

M-101-C

VERSION

1

CODIGO DE PROYECTO

HND_0067